



# PORTFOLIO

Adiba Yesmin Chowdhury


| Resume Summary   |                                                     | Table of Contents                       |       |
|---|-----------------------------------------------------|-----------------------------------------|-------|
| <b>Education</b>   |                                                     | Beyond The Grid                         | 01-02 |
| The City College of New York<br>Master of Landscape Architecture (MLA) (2024-2027)   |                                                     | Between the Neighborhoods               | 03-04 |
| Ahsanullah University of Science and Tecnology<br>Bachelor of Architecture (B. Arch.) (2015-2021)   |                                                     | Redesign of Ashrafi Masjid              | 05    |
| <b>Work Experience</b>   |                                                     | Design of a Community Mosque            | 06    |
| City College of New York- New York<br>- College Assistant (2025-Present)   |                                                     | Game Ready Assets                       | 07    |
| 'Attrito M7 Productions' - Dhaka, Bangladesh<br>- Junior Level Architect (2022-2023)   |                                                     | Sketches                                | 08    |
| <ul style="list-style-type: none"><li>Key responsibilities: modeling and texturing of video game environments &amp; assets</li><li>Video games contributed to: Mayhem, Pink Slip Midnight</li></ul>   |                                                     | Interior Design of an Apartment         | 09-10 |
| 'Architects' - Dhaka, Bangladesh<br>- Junior Assistant Architect (2021-2022)   |                                                     | Design of Ahsania Mission Children City | 11-12 |
| <ul style="list-style-type: none"><li>Key responsibilities: architectural design, interior design, landscape design, working drawing, furniture design, 3D visualization, project supervision</li><li>Projects contributed to: Dadanpur Munshipara Zame Mosque, BBS Interior, Site Office of Indigo Marble, Landscape Design of Manikgang Graveyard</li></ul> |                                                     | AutoCAD Technical Drawing               | 13-14 |
| <b>Skills</b>   |                                                     | ArcGIS Mapping and Spatial Analysis     | 15-16 |
| Design and Rendering   | AutoCAD, Lumion, V-Ray                              |                                         |       |
| 3D Design and Sculpting   | Rhino, SketchUp, Maya, ZBrush                       |                                         |       |
| Visual programming   | Grasshopper                                         |                                         |       |
| Graphics and Editing   | Photoshop, InDesign, Illustrator, Substance Painter |                                         |       |
| Geospatial Platform   | ArcGIS Pro                                          |                                         |       |
| Microsoft Office   | Word, Excel, PowerPoint, Teams, Outlook             |                                         |       |
| Google Workspace   | Docs, Sheets, Slides                                |                                         |       |
| Photogrammetry Software   | Substance Alchemist                                 |                                         |       |




# Beyond The Grid

Yadiel Rivera-Diaz & Juan Guzman-Palacios, MLA, Studio II -Spring 2025


It was a concept project where we learned how to develop a manifesto and a framework for a project. I worked with a partner on this. Our main idea was “rewilding urban spaces.” We analyzed Northern Manhattan and created some vignettes based on our idea.

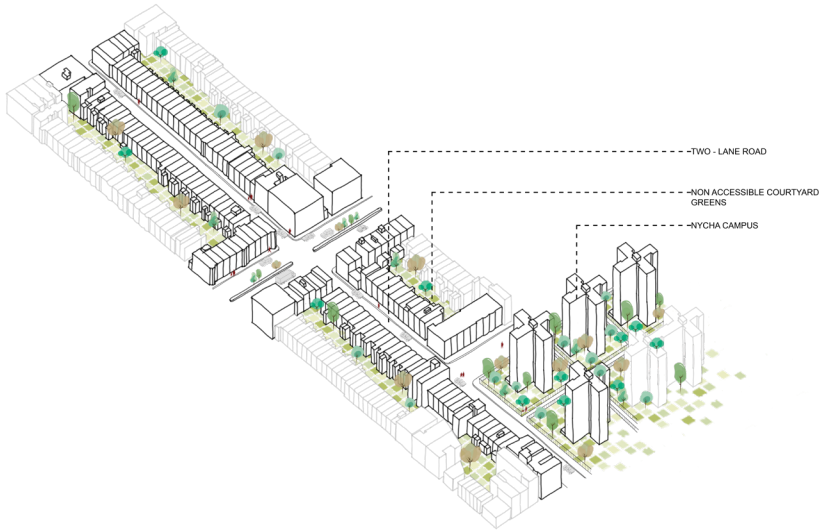


Axonometric Drawing (Existing Condition)

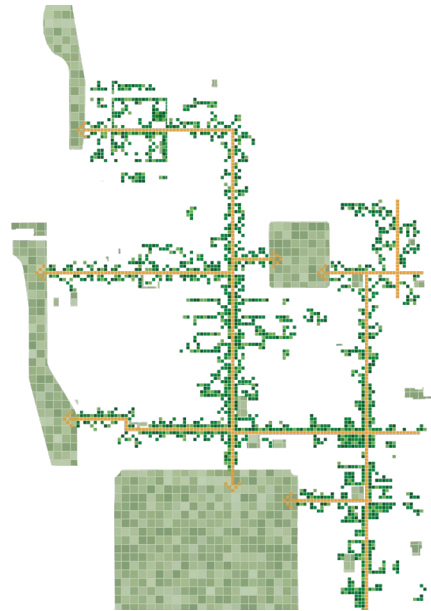


Framework

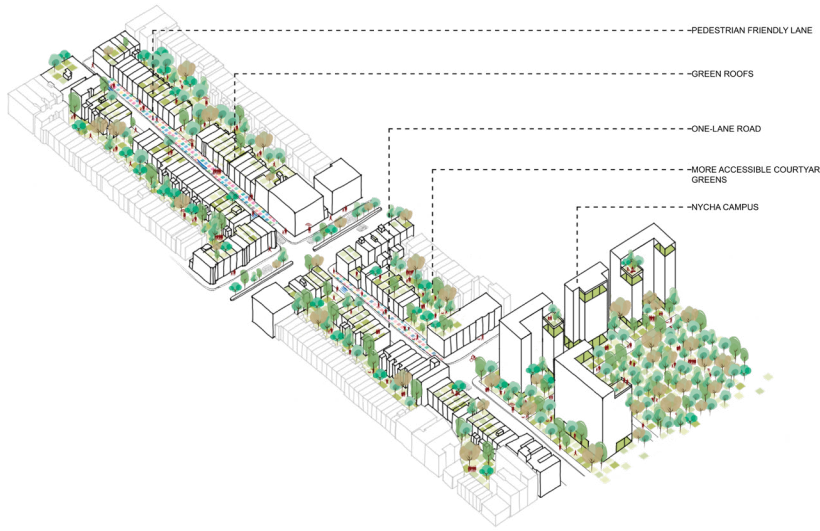

Axonometric Drawing (Proposed Design)

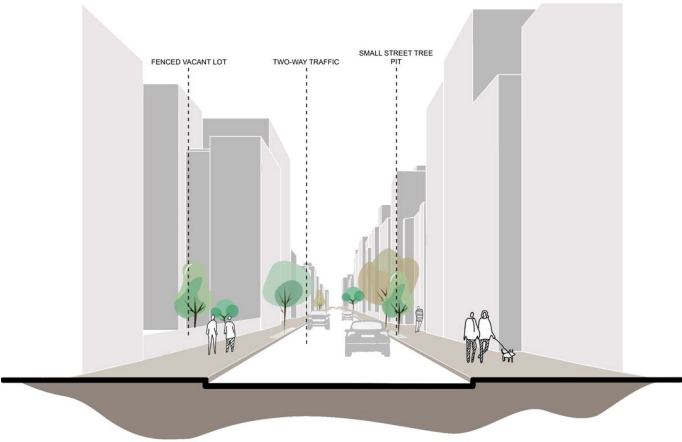


Section (Existing Condition)

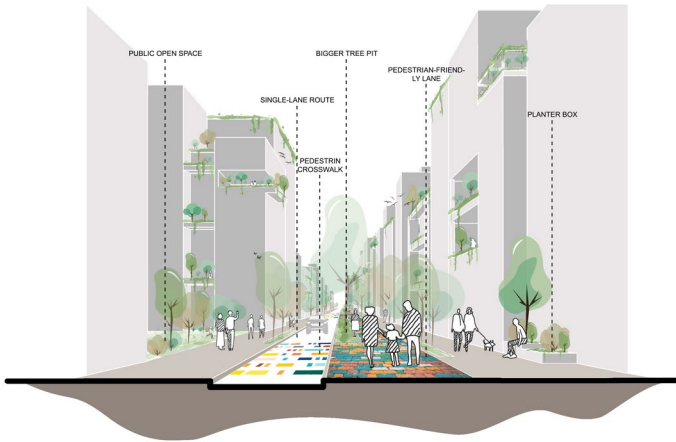

Section (Proposed Design)

# Beyond The Grid

This is the proposed design from 5th Avenue to Marcus Garvey Park, and to implement this design, we used the Miyawaki forest method and Desvigne's grid planting method for planting.

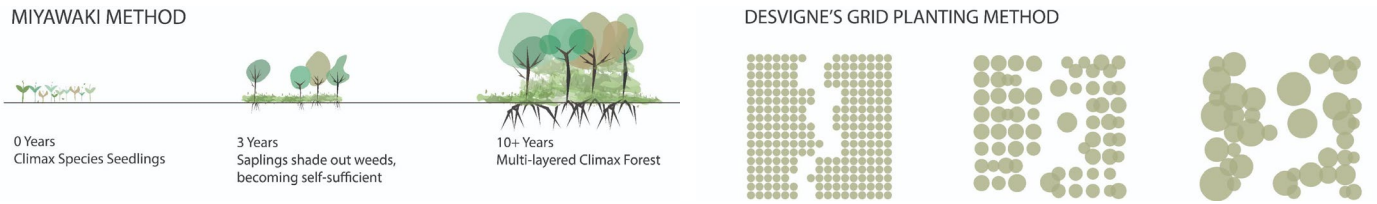

Planting Methods



Proposed Design




# Between the Neighborhoods

Michael King, MLA Foundations Studio -Fall 2024


In this studio project, I worked with a partner to redesign a site in Manhattan. We picked the site by looking for a location between where both of us live. We chose the pedestrian alley on E. 27th Street, between Mt. Carmel Place and 1st Avenue. One side of the street connects to Bellevue Hospital, and the other side leads to Bellevue South Park. This alley is often used by pedestrians and bikers, but there is no seating available. Our idea was to improve the space by adding different types of seating, increasing the size of planting areas, and making it a more welcoming place where people can stop and gather. We kept the large trees already there and added plants in the under-story and ground layer. We designed various seating, including benches, ledges, and movable tables with chairs. We also included space for vendors to serve people from the hospital and the nearby neighborhood.



3D Visualizations

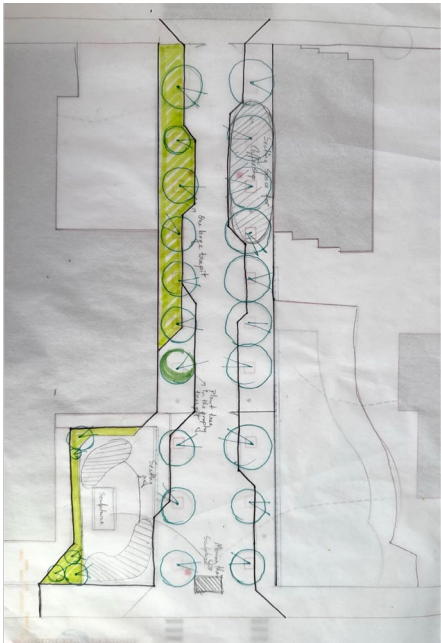


Preliminary Concept Drawing

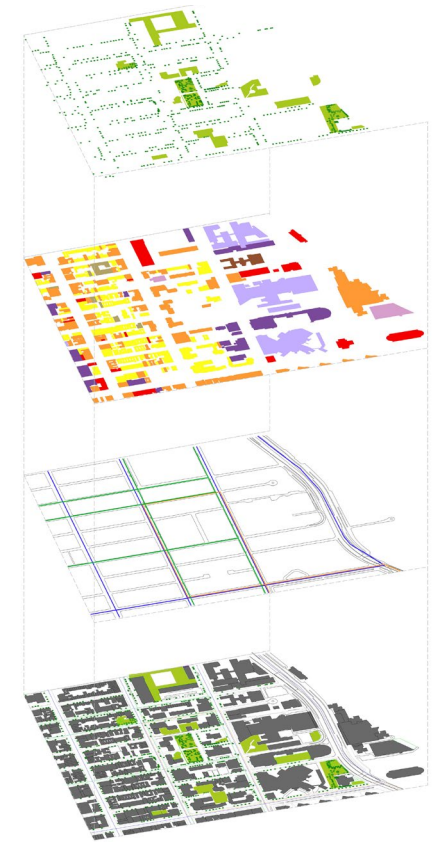

Layered Plan

# Between the Neighborhoods

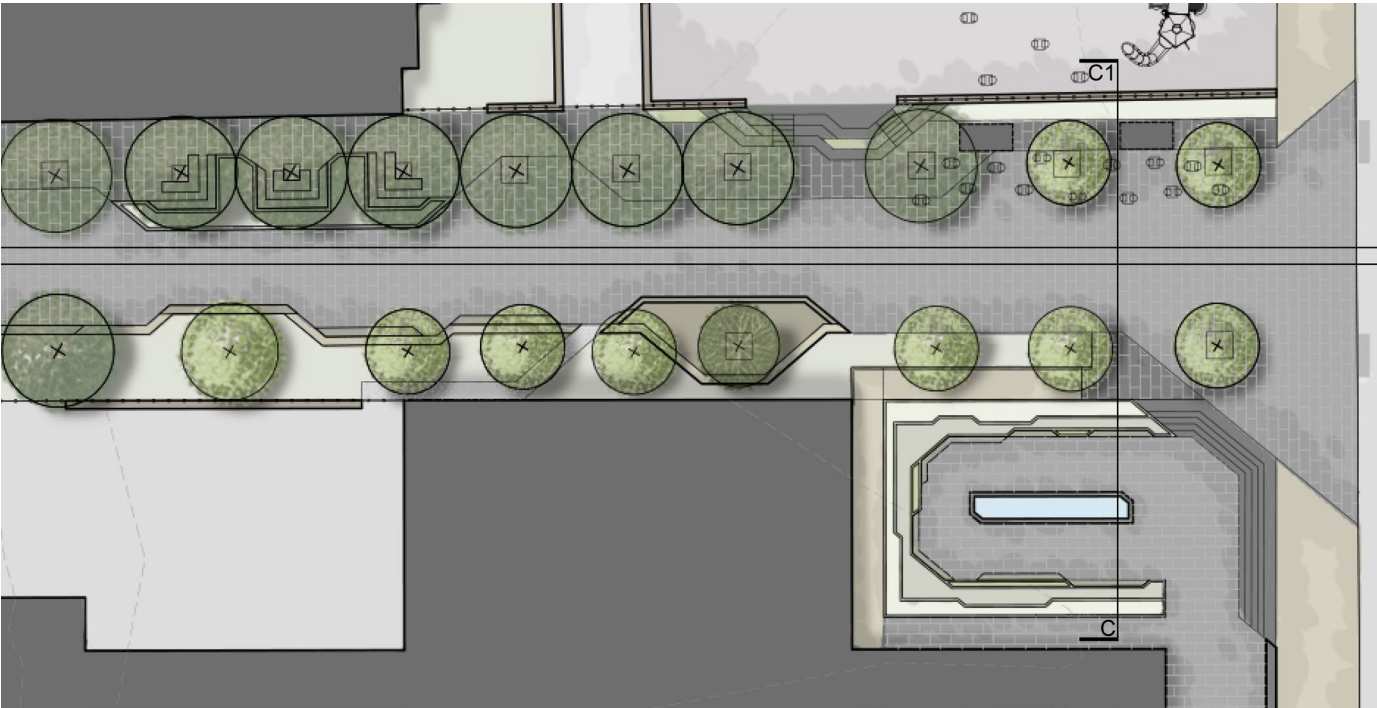

Plan



Section C-C1



Tools Used - Hand Sketch, AutoCAD, Adobe suite, Sketch Up



# Redesign of Ashrafi Masjid - Karachi, Pakistan

Freelance Project

## Project Information

The project involved a redesign based on the client's desire for the mosque to resemble The Blue Mosque in Turkey. Additionally, the client specified the inclusion of residential facilities for the imam and muazzin, along with their families. The entrance to the residential area needed to be distinct. Other essential elements included designated spaces for ablution, janajah gah, and public toilets.



3D Visualization




3D Visualization

# Design of a Community Mosque - Bangladesh

Architects

## Project Information

The client requested a community mosque with maximum prayer space and housing for the Imam and Muazzin, with the main challenge being the concrete screen design on the first floor.

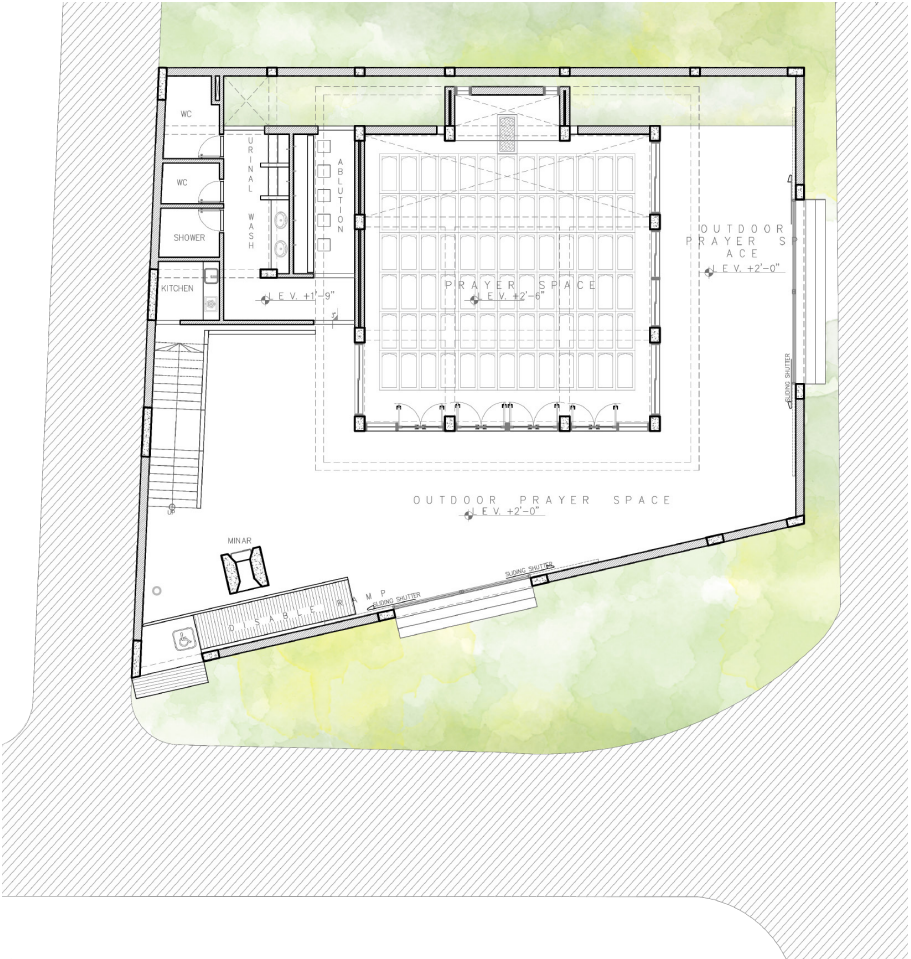

Ground Floor Plan



Images from Under Construction Site



3D Visualization




3D Visualization



Project Information


The project began with a simple low-poly model in SketchUp, which was refined in ZBrush into a detailed high-poly version. Textures and materials were created from scratch in Substance 3D Painter to give the model a unique look. The high-poly details were then baked onto the low-poly version in Maya, balancing performance and realism. The main challenge was minimizing textures, solved by using a custom trim sheet of 7–10 textures designed specifically for the building.

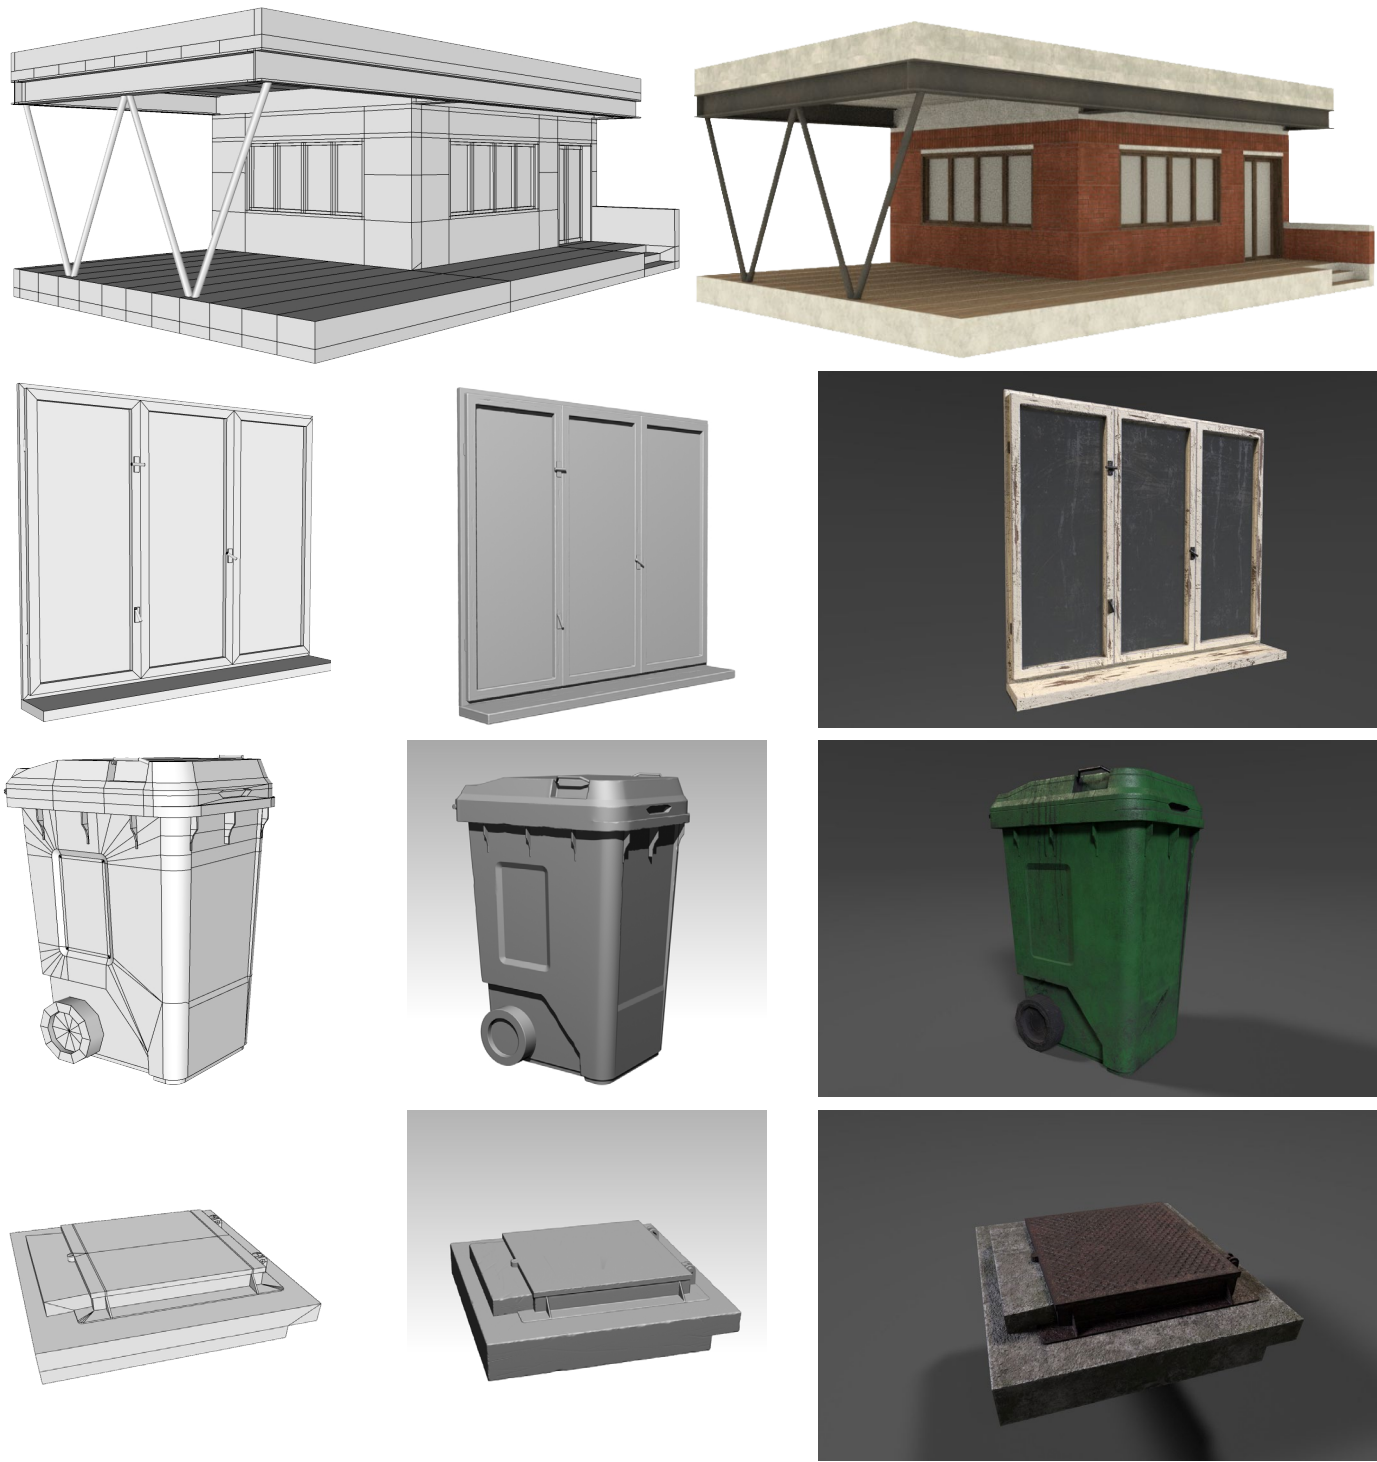




# Interior Design of an Apartment - Sylhet, Bangladesh

Freelance Project

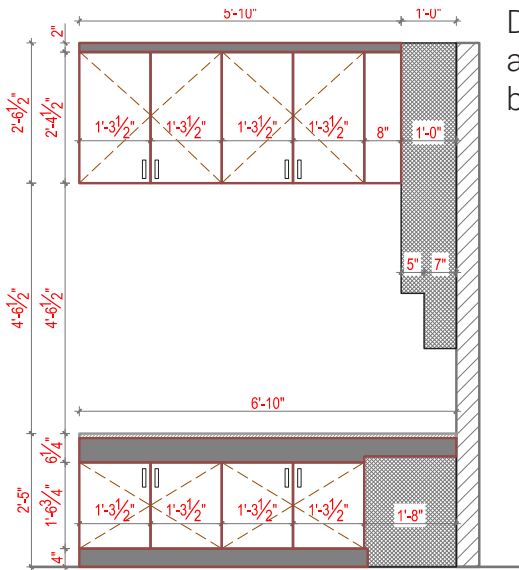

FRONT ELEVATION OF C7  
SCALE: AS SHOWN

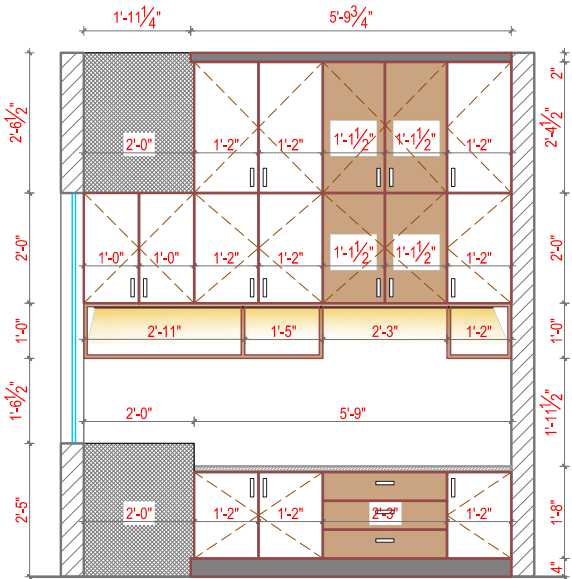

SIDE ELEVATION OF C7  
SCALE: AS SHOWN

Designed the interior layout and custom furniture for a residential apartment, focusing on making the space practical and visually balanced.



3D Visualization



# Interior Design of an Apartment - Dhaka, Bangladesh

Freelance Project

## Project Information

This interior project was a small family apartment. I was tasked with creating a straightforward and minimalist interior. The client specifically requested that the design not be overwhelmed with materials or colors. The main challenge was blending the new design with the existing furniture. Given the limited space of the apartment, I opted for brown color palette to enhance the perception of spaciousness in the room.



3D Visualization



Images from Under Construction Site




# Design of Ahsania Mission Children City

B. Arch. - Fourth Year, First Semester (Spring 2018)

## Project Information


This project aims to provide support and care for destitute and orphaned children, offering them a safe haven and opportunities for a better future. It focuses on addressing their needs, including shelter, education, and emotional well-being, fostering a nurturing environment for these vulnerable children to thrive.

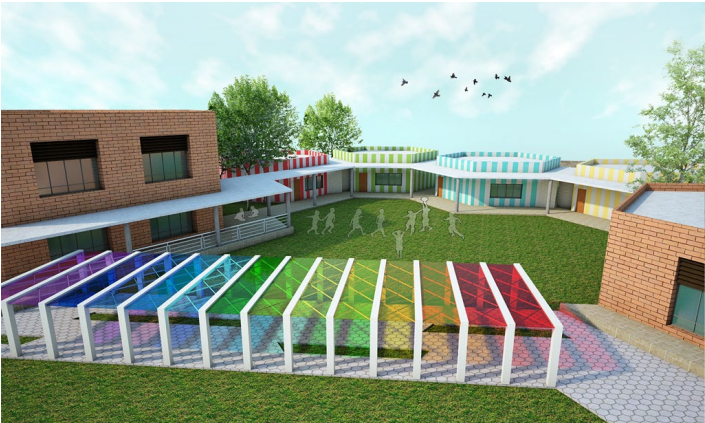

3D Visualization




3D Visualization

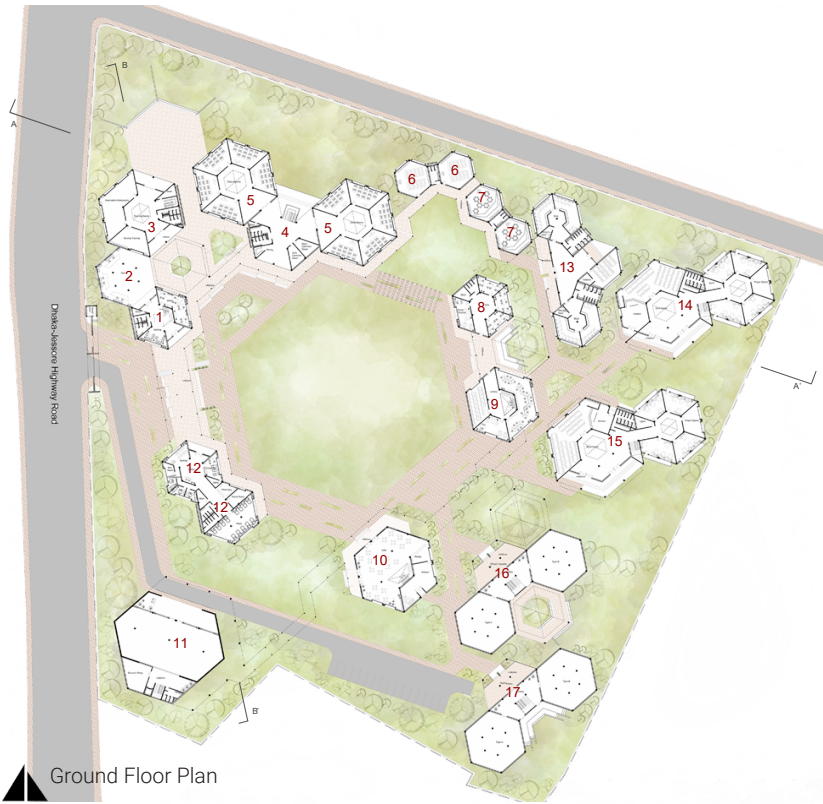

Ground Floor Plan

### Legend

- |                    |                       |
|--------------------|-----------------------|
| 1. Admin Block     | 10. Cafeteria         |
| 2. Sells Center    | 11. Exhibition Space  |
| 3. Training Center | 12. Medical Center    |
| 4. Academic Block  | 13. Dorm              |
| 5. Academic Block  | 14. Girl's Hostel     |
| 6. Primary School  | 15. Boy's Hostel      |
| 7. Pre-School      | 16. Teacher's Quarter |
| 8. Teachers Block  | 17. Staff's Quarter   |
| 9. Library         |                       |

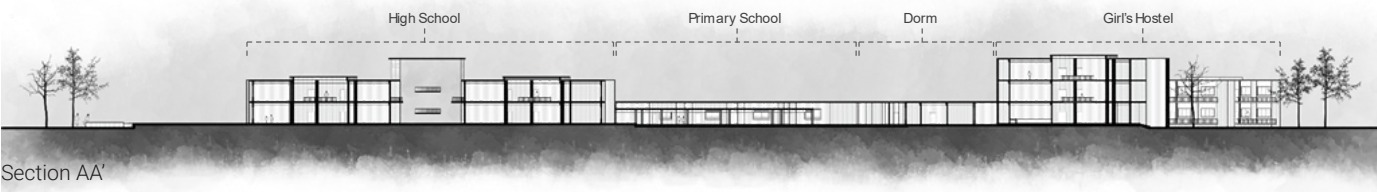

Section AA'

# Design of Ahsania Mission Children City



Image of model



Image of model



### Legend

- |                    |                       |
|--------------------|-----------------------|
| 1. Admin Block     | 14. Girl's Hostel     |
| 3. Training Center | 15. Boy's Hostel      |
| 4. Academic Block  | 16. Teacher's Quarter |
| 5. Academic Block  | 17. Staff's Quarter   |
| 9. Library         | 18. Multipurpose Hall |
| 10. Cafeteria      |                       |




North Elevation




West Elevation



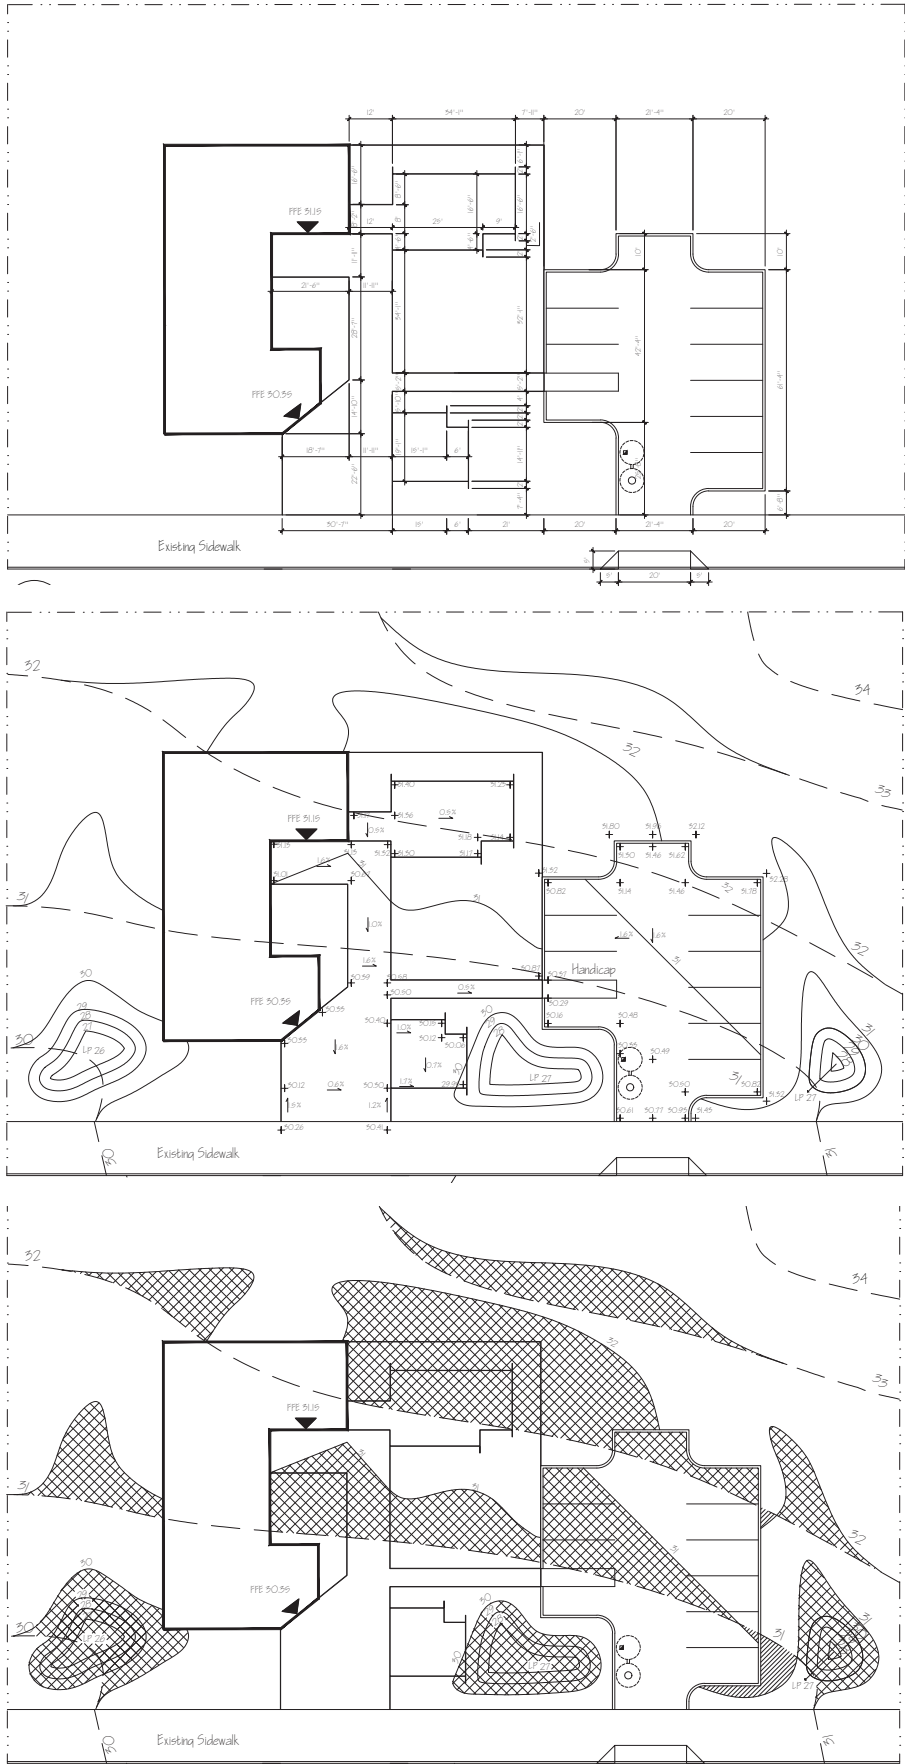


This course focused on the technical side of drawing. I learned how to create grading plans, calculate cut and fill, make material and planting plans, and draw construction details that are needed to build a project.

LEGEND

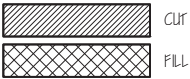

| CUT AND FILL CHART        |                 |              |
|---------------------------|-----------------|--------------|
| CONTOUR                   | CUT             | FILL         |
| 33                        | 856.72 SQFT     | 0 SQFT       |
| 32                        | 3256.17 SQFT    | 0 SQFT       |
| 31                        | 3192.97 SQFT    | 13.44 SQFT   |
| 30                        | 639.76 SQFT     | 160.61 SQFT  |
| TOTAL (SQFT)              | 7945.62 SQFT    | 174.05 SQFT  |
| TOTAL SQ FT X CONTOUR     | 7945.62 X 1     | 174.05 X 1   |
| INTERVAL=TOTAL CU FT      | 7945.62 CU FT   | 174.05 CU FT |
| PAVEMENT EXCAVATION       |                 |              |
| ASPHALT                   | 2404.53 CU FT   | 0            |
| CONCRETE                  | 1306.38 CU FT   | 0            |
| PERMEABLE                 | 1368.17 CU FT   | 0            |
| BIORETENTION AREA (CU FT) |                 |              |
|                           | 712.04 + 217.82 | 0            |
|                           | + 548.01 =      |              |
|                           | 1477.87 CU FT   |              |
| TOTAL CU FT / 27          | 14502.57 / 27   | 174.05 / 27  |
| = TOTAL (CU YD)           | = 537.13 CU YD  | = 6.45 CU YD |

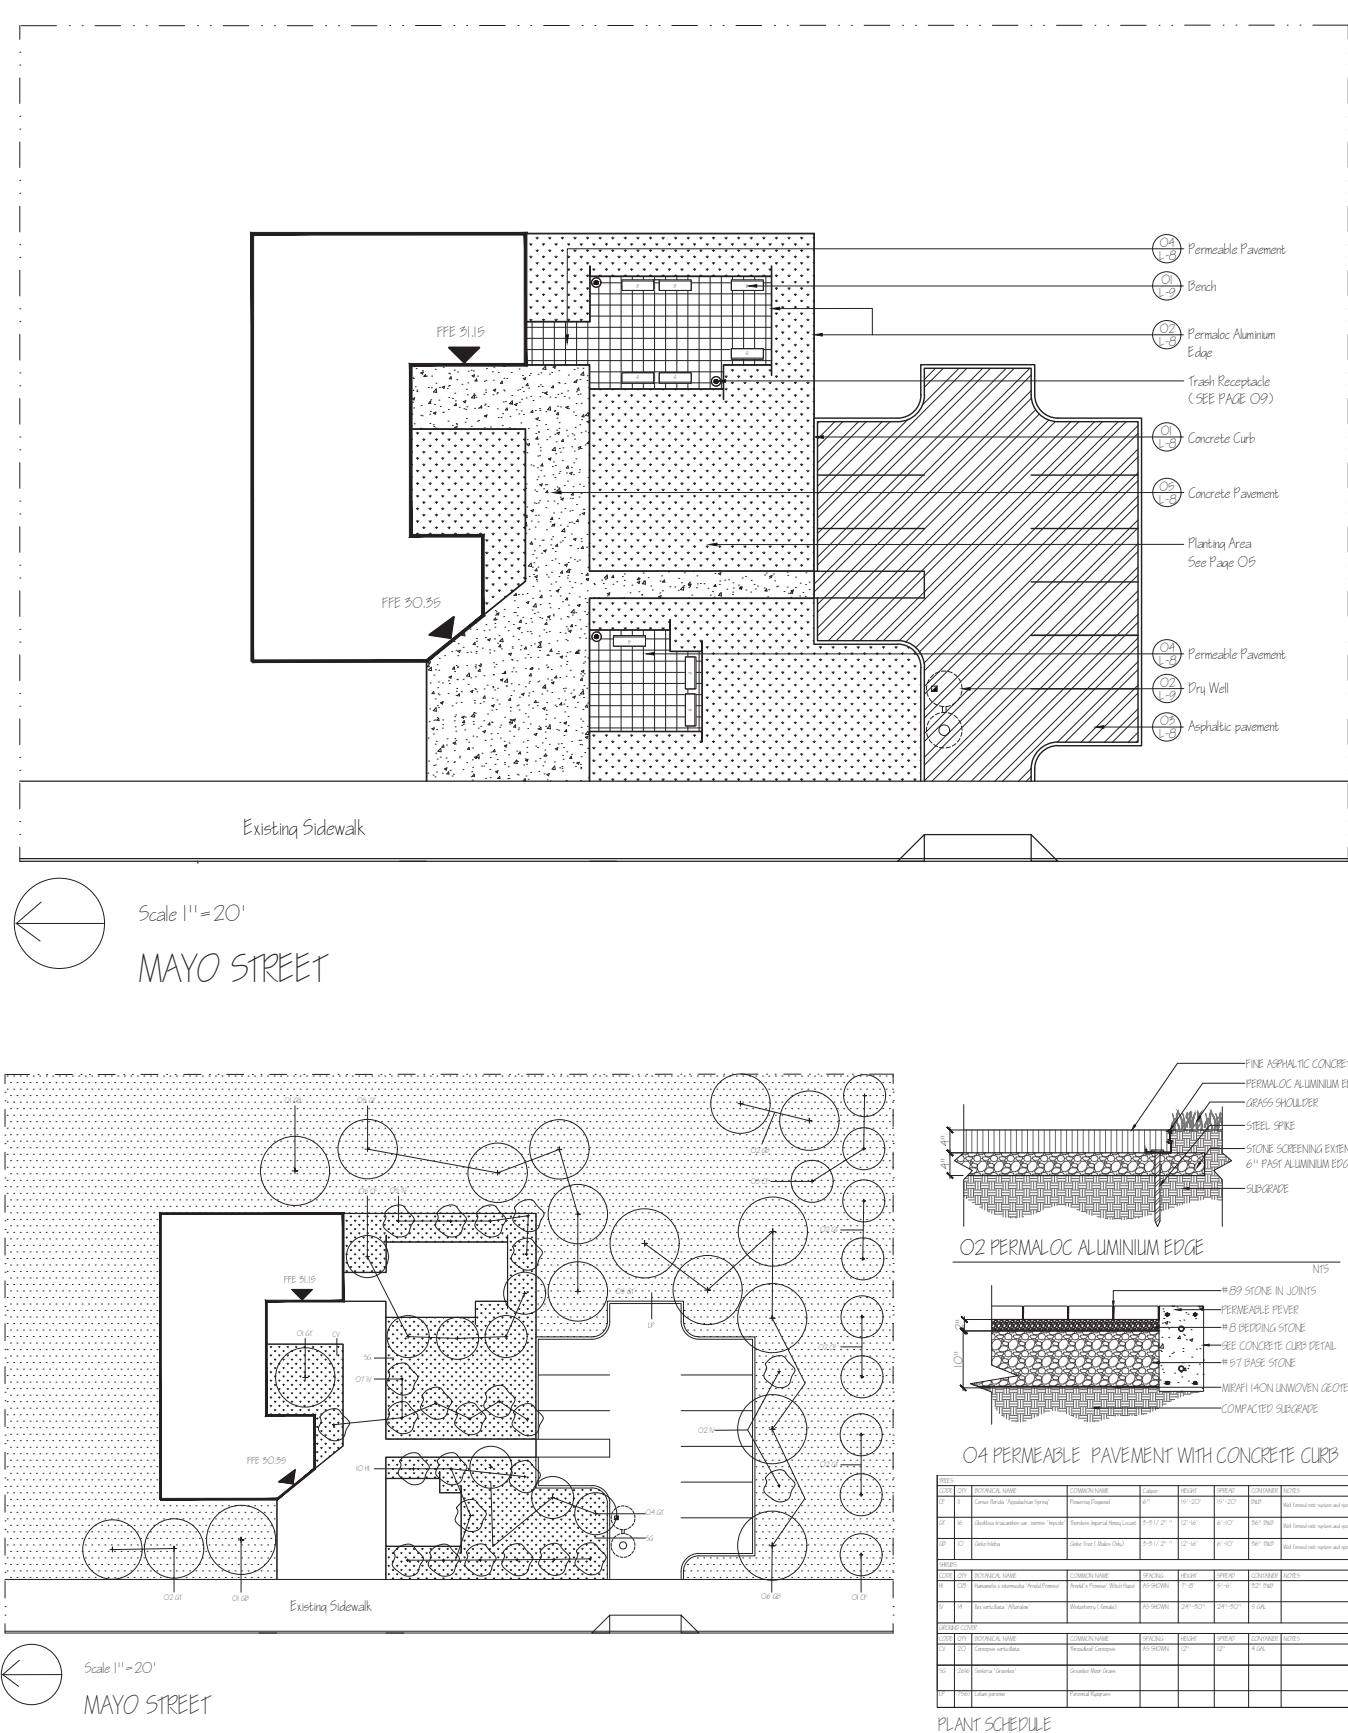





# ArcGIS Mapping and Spatial Analysis

Michael Tantala, Urban Ecology -Spring-2025


In this project, I looked at the road network of Dhaka and how it connects to schools and hospitals. I also studied the new MRT (Metro Rail) line and how it helps improve access to these public services. Using GIS, I mapped where schools and hospitals are located and how close they are to roads and MRT stations.

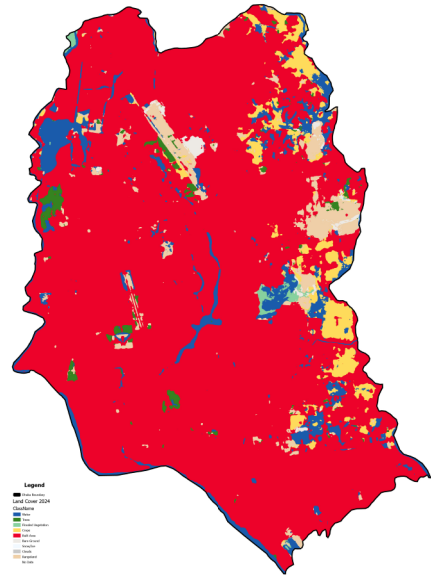

Land Cover Map

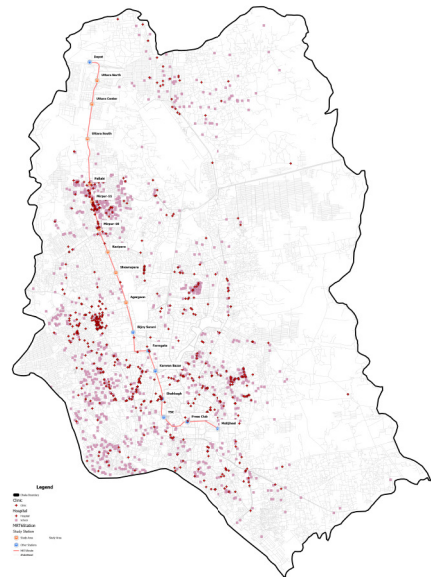

Road Network Map

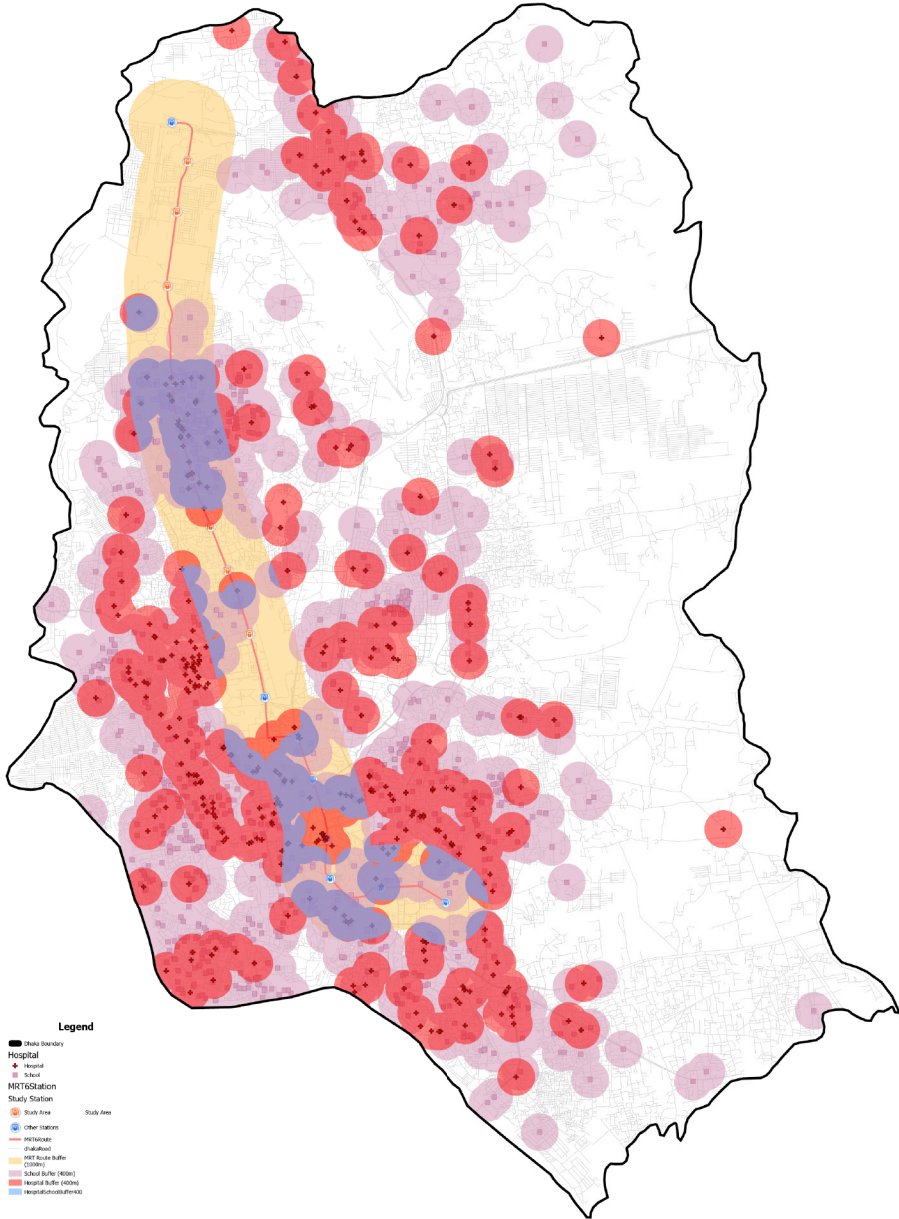


Schools, Hospital and MRT Intersection Map


# ArcGIS Mapping and Spatial Analysis

Michael Tantala, Urban Ecology -Spring-2025


In this project, I analyzed crime locations in ZIP code 11377, Queens, NYC. I looked at how close schools are to those crime spots. I also studied the topography and water flow (hydrology) of the area to better understand the surroundings.

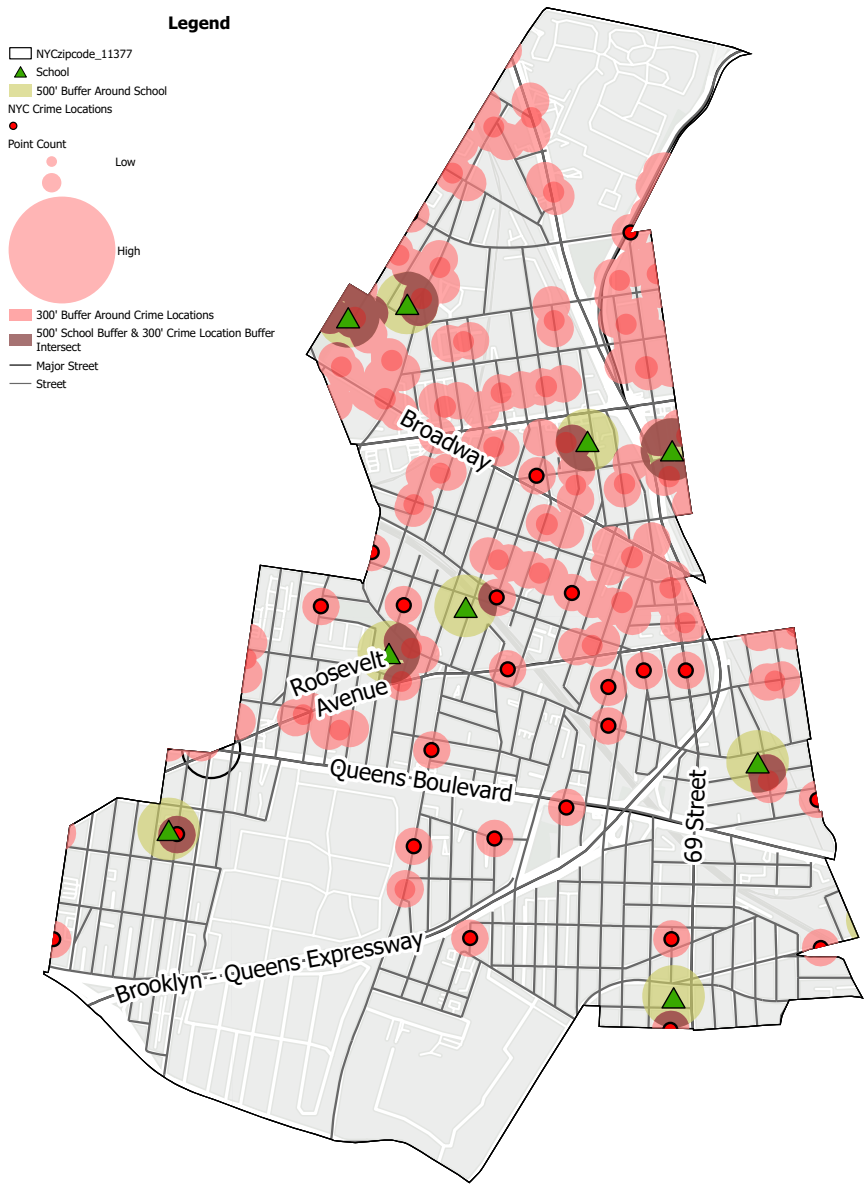

Crime Location Intersection with Schools Map

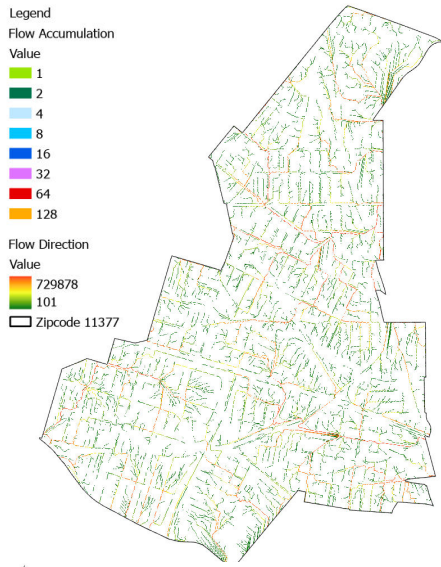

Hydrology Map

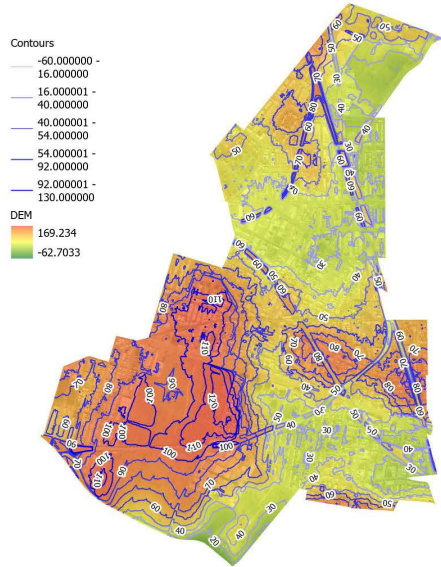

Topography Map